




Юридический отдел
Инв. № подл.
Подп. и дата
Взам. инв. №
Инв. № дубл.
Подп. и дата

Подп. и дата

Спроб. №

Перв. примен.

05.23932.00 СБ

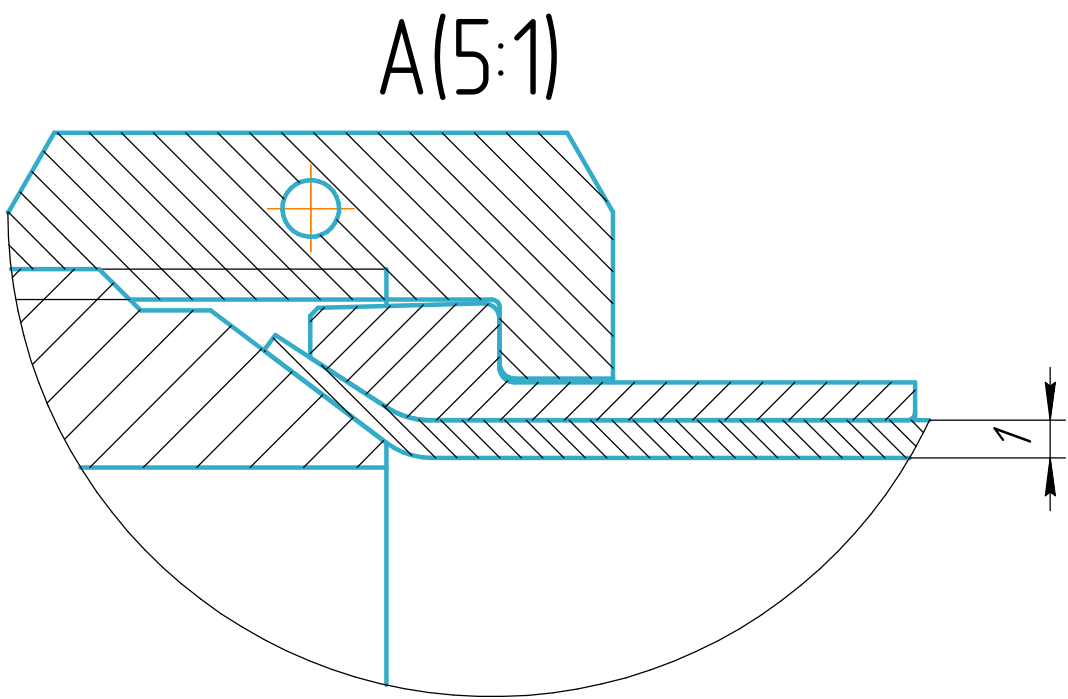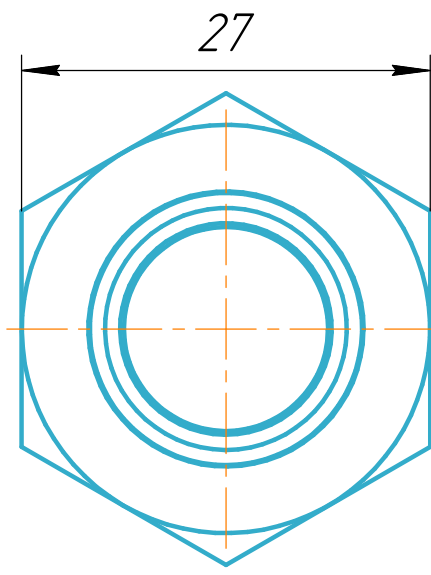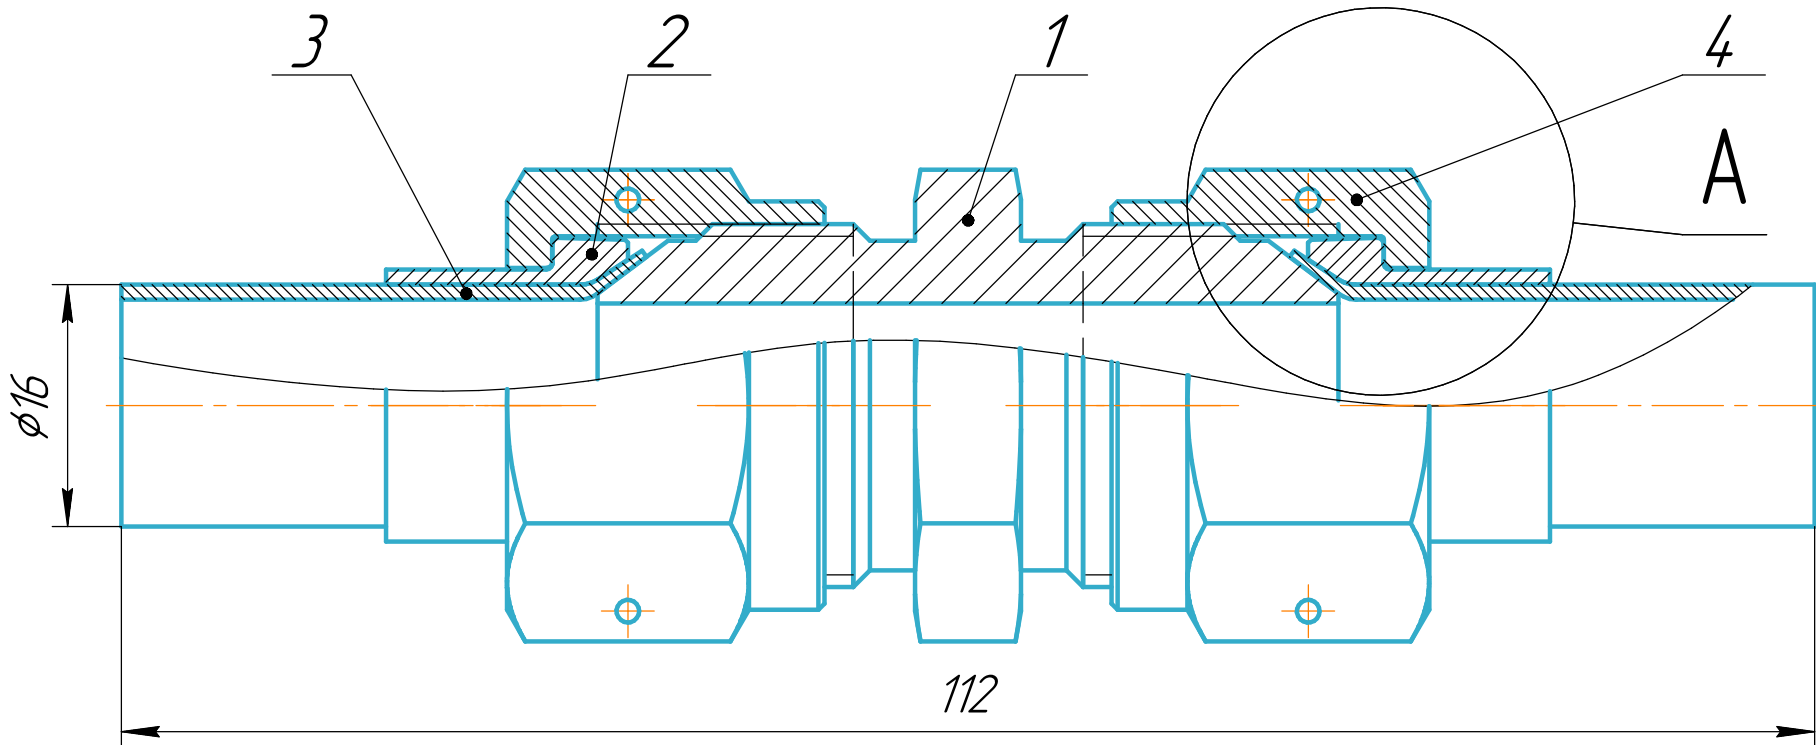

Формат	Зона	Поз.	Обозначение	Наименование	Кол.	Примечание
				Детали		
A4		1	05.23932.001	Проходник прямой 16-13А ГОСТ 13959-74	1	
A4		2	05.23932.002	Ниппель 1-16-13А ГОСТ 13956-74	2	
A4		3	05.23932.003	Труба 16х1-12Х18Н10Т ГОСТ 9941-81	2	
A4		4	05.23932.004	Гайка накидная 16 - 13А ГОСТ 13957-74	2	
05.23932.00 СБ						
Изм. Лист			№ докум.	Подп.	Дата	Соединение трубопроводов по наружному конусу ГОСТ 13977-74 Сборочный чертеж
Разраб.			Карпачев		03.03	
Пров.						
Т.контр.						
Н.контр.						Лит. 8 Листов 36
Утв.						
Копировал						НГУ-2026
Формат А3						